Propriété dite : Ard Dar El Knatar

Située à : Pce d'EL JADIDA, Cle de SIDI SMAIL, Cne. Mogress, Dr LAHRICHATE

Titre :

Echelle : 1/500

Plan levé en : Mai 2025

Limite de la propriété

Réquisition N° :

S7 25


NORD الشمال

Plan Provisoire Avant enrôlement

Plle n° : 6797

IFE : Zone Mogress

Sous zone : 3

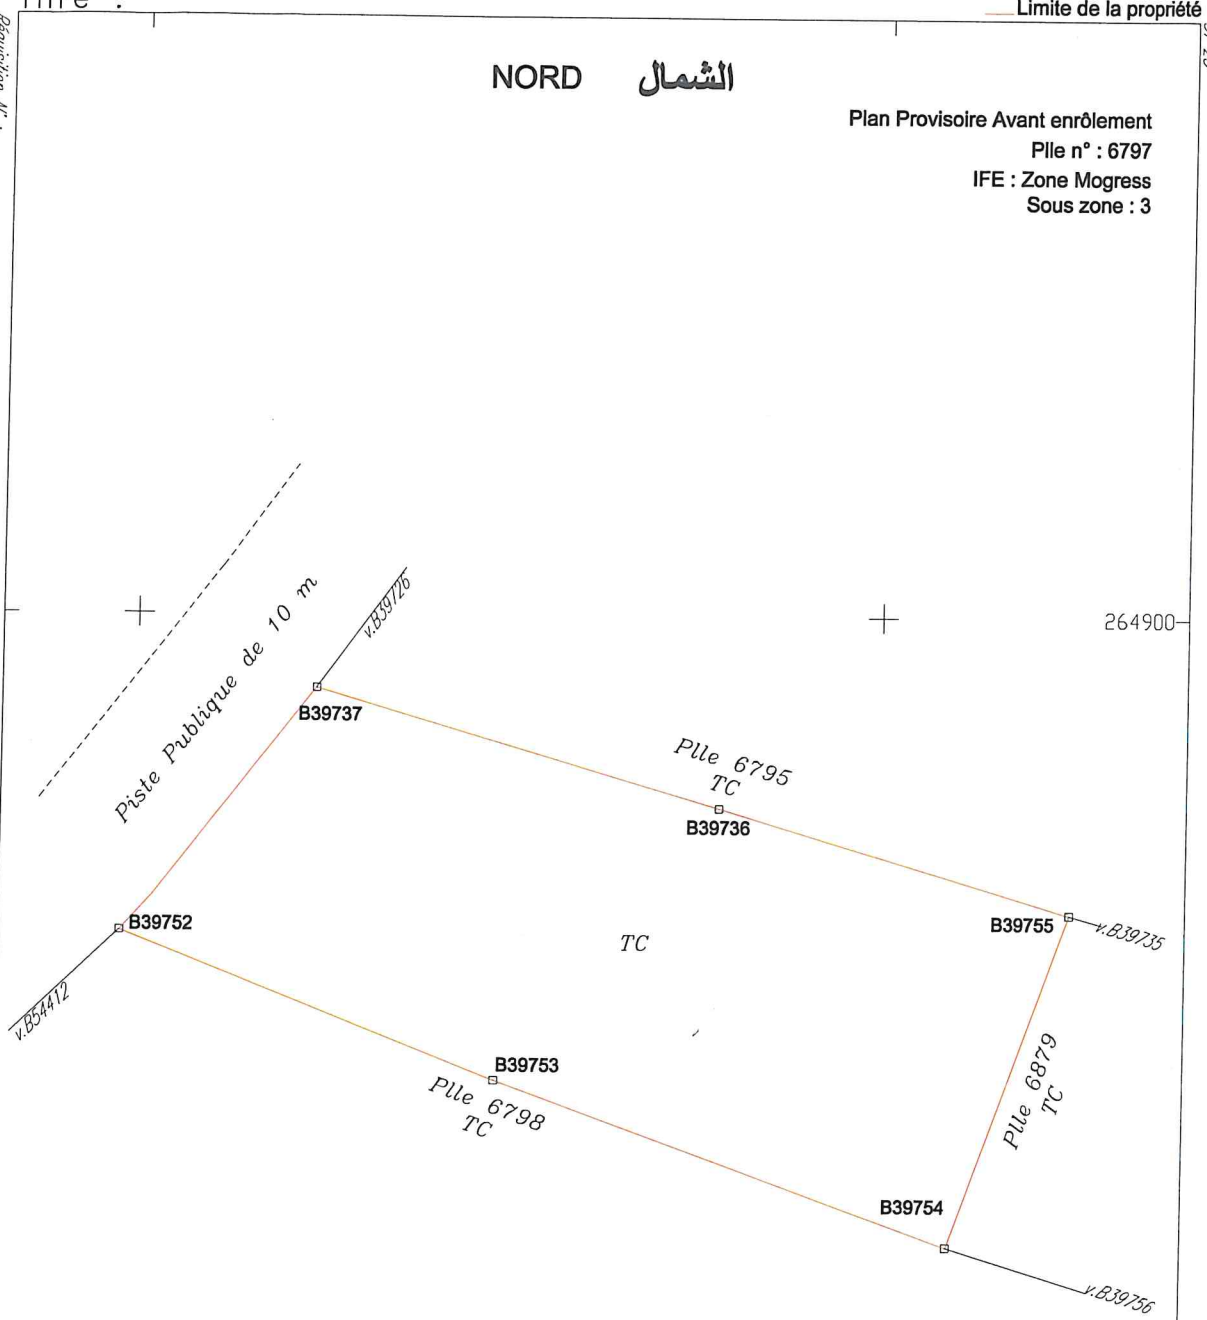

Contenance : 12^{A} 27^{Ca} : مساحة

213100

213150

23-12-99-f

الملك المسمى :ارض دار القناطر

الكائن ب :إقليم الجديدة دائرة سيدي اسماعيل جماعة مكرس دوار الحريشات

رسم :

مطلب عدد:

DIRECTION
DU CADASTRE

Plan établi par : GEOXPER
Géomètre : MJOUEL Mohamed Amjad
Dessinateur : Automatique

MAPPE DE REPERAGE AU 1/2000 : 23-12-99
CARTE TOPOGRAPHIQUE DE SOUK ARBAA MOGRESS au 1/50000

Propriété dite : Ard Dar El Knatar

Située à : Pce d'EL JADIDA, Cle de SIDI SMAIL, Cne. Mogress, Dr LAHRICHATE

Titre :

Echelle : 1/500

Plan levé en : Mai 2025

Limite de la propriété

Réquisition N° :

ST 26

NORD الشمال

Plan Provisoire Avant enrôlement

Plle n° : 6801

IFE : Zone Mogress

Sous zone : 3

B39747 B39746 B39745 B39744 B39743 B39742

B39748 B39767 B39768 B39769 B39770 B39771

Plle 6796 TC

Plle 6802 TC

Plle 6803 TC

Plle 6804 TC

Plle 6805 TC

Plle 6806 TC

Plle 6826 TC

Plle 6827 TC

Plle 6829 TC

TC

v.B39749 v.B39778 v.B39777 v.B39775 v.B39774 v.B39772 v.B39879 v.B39882

264800

264750

213150 213200 213250

Contenance : $30^{A}\ 80^{Ca}$: مساحة

23-12-99-f

DIRECTION DU CADASTRE

Plan établi par : GEOXPER
Géomètre : MJOUEL Mohamed Anjod
Dessinateur : Automatique

MAPPE DE REPERAGE AU 1/2000 : 23-12-99
CARTE TOPOGRAPHIQUE DE SOUK ARBAA MOGRESS au 1/50000

مطلب عن :

الملك المسمى :ارض دار القناطر

الكائن بـ :اقليم الجبيدة دائرة سيدي اسماعيل جماعة مكرس دوار الحريشات

رسم :

Propriété dite : Ard El Hatta

Située à : Pce d'EL JADIDA, Cle de SIDI SMAIL, Cne. Mogress, Dr LAHRICHATE

Titre :

Echelle : 1/500

Plan levé en : Mai 2025

Limite de la propriété

Réquisition N. :

ST 25

NORD الشمال

Plan Provisoire Avant enrôlement

Plle n° : 6972

IFE : Zone Mogress

Sous zone : 3

264500

264450

264400

212750

212800

v.B42889

Plle 6974 TC

B42901

B42908

v.B42917

B42902

B42907

L.E.B.T TC

Plle 6971 TC

Plle 6973 TC

B42903

B42906

v.B42886

B42904

B42905

Chemin de LV

v.B42910

Contenance : $03^{A}\ 77^{Ca}$: مساحة

23-12-99

DIRECTION DU CADASTRE

Plan établi par : GEOXPER

Géomètre : MJOUEL Mohamed Amjad

Dessinateur : Automatique

MAPPE DE REPERAGE AU 1/2000 : 23-12-99

CARTE TOPOGRAPHIQUE DE SOUK ARBAA MOGRESS au 1/50000

مطلب عدد :

الملك المسمى :ارض الحطة

الكائن ب :اقليم الجديدة دائرة سيدي اسماعيل جماعة مكرس دوار الحريشات

رسم :

Propriété dite : Ard El Oued

Située à : Pce d'EL JADIDA, Cle de SIDI SMAIL, Cne. Mogress, Dr LAHRICHATE

Titre :

Echelle : 1/500

Plan levé en : Mai 2025

Limite de la propriété

Réquisition N° :

ST 26

NORD الشمال

Plan Provisoire Avant enrôlement
Plle n° : 11039
IFE : Zone Mogress
Sous zone : 3

264100

piste publique de 10 m

v.B43812

B43822

B43823

Plle 11040
TC

B43821

v.B43809

B43820

B43824

TC

B43819

Plle 11038
TC

B43825

B43818

v.B43827

B43826

B43817

oued

B43816

v.B43815

264050

264000

Contenance : $16^{A}\ 31^{Ca}$: مساحة

212900

212950

213000

23-12-99-n

DIRECTION
DU CADASTRE

Plan établi par : GEOXPER
Géomètre : MJOUEL Mohamed Amjad
Dessinateur : Automatique

MAPPE DE REPERAGE AU 1/2000 : 23-12-99
CARTE TOPOGRAPHIQUE DE SOUK ARBAA MOGRESS au 1/50000

مطلب عدد:

الملك المسمى :ارض الواد

الكائن ب :إقليم الجديدة دائرة سيدي اسماعيل جماعة مكرس دوار الحريشات

رسم:

Propriété dite : Ard El Mezara

Située à : Pce d'EL JADIDA, Cle de SIDI SMAIL, Cne. Mogress, Dr LAHRICHATE

Titre :

Echelle : 1/1000

Plan levé en : Mai 2025

Limite de la propriété

Réquisition N° :

ST 25

NORD الشمال

Plan Provisoire Avant enrôlement

Plle n° : 6849

IFE : Zone Mogress

Sous zone : 3

v.B40490

Plle 6847 TC

B40493

B40492

B40491

Plle 6942 TC

v.B40495

B40494

B40504

v.B42453

264500

Plle 6939 TC

B40505

B40503

Plle 6941 TC

TC

B40502

v.B42443

B40506

v.B40500

B40501

Plle 6940 TC

Chemin Public de LV

B40507

v.B42452

264400

Contenance : 38^A 87^Ca : مساحة

213200

213300

23-12-99-C

مطلب عدد:

رسم:

الملك المسمى :ارض المزارة

الكائن ب :اقليم الجديدة دائرة سيدي اسماعيل جماعة مكرس دوار الحريشات

DIRECTION DU CADASTRE

Plan établi par : GEOXPER
Géomètre : MJOUEL Mohamed Amjad
Dessinateur : Automatique

MAPPE DE REPERAGE AU 1/2000 : 23-12-99
CARTE TOPOGRAPHIQUE DE SOUK ARBAA MOGRESS au 1/50000

Propriété dite : Ard Tres

Située à : Pce d'EL JADIDA, Cle de SIDI SMAIL, Cne. Mogress, Dr LAHRICHATE

Titre :

Echelle : 1/1000

Plan levé en : Mai 2025

Limite de la propriété

Réquisition N° :

ST 25

NORD الشمال

Plan Provisoire Avant enrôlement
Plle n° : 6993
IFE : Zone Mogress
Sous zone : 3

265200

265100

265000

212700

212800

v.B43197

v.B41852

Plle 6992 TC

B43210

B41853

B43211

Plle 6911 TC

B41854

B43212

Hiers Fatna Dounoune TC

TC

B41843

B43213

v.B41842

B41844

Plle 6910 TC

B43214

B43215

B41845

B41846

Mohammed Dounoune TC

v.B41847

Contenance : 33^A 89^Ca : مساحة

23-12-99-A

الملك المسمى : ارض تريس

الكائن ب : اقليم الجديدة دائرة سيدي اسماعيل جماعة مكرس دوار الحريشات

رسم :

مطلب عدد :

DIRECTION DU CADASTRE

Plan établi par : GEOXPER
Géomètre : MJOUEL Mohamed Amjad
Dessinateur : Automatique

MAPPE DE REPERAGE AU 1/2000 : 23-12-99
CARTE TOPOGRAPHIQUE DE SOUK ARBAA MOGRESS au 1/50000

Propriété dite : Ard El Hofra

Située à : Pce d'EL JADIDA, Cle de SIDI SMAIL, Cne. Mogress, Dr LAHRICHATE

Titre :

Echelle : 1/1000

Plan levé en : Mai 2025

Limite de la propriété

Réquisition N° :

ST 25


NORD الشمال

Plan Provisoire Avant enrôlement

Plle n° : 6940

IFE : Zone Mogress

Sous zone : 3

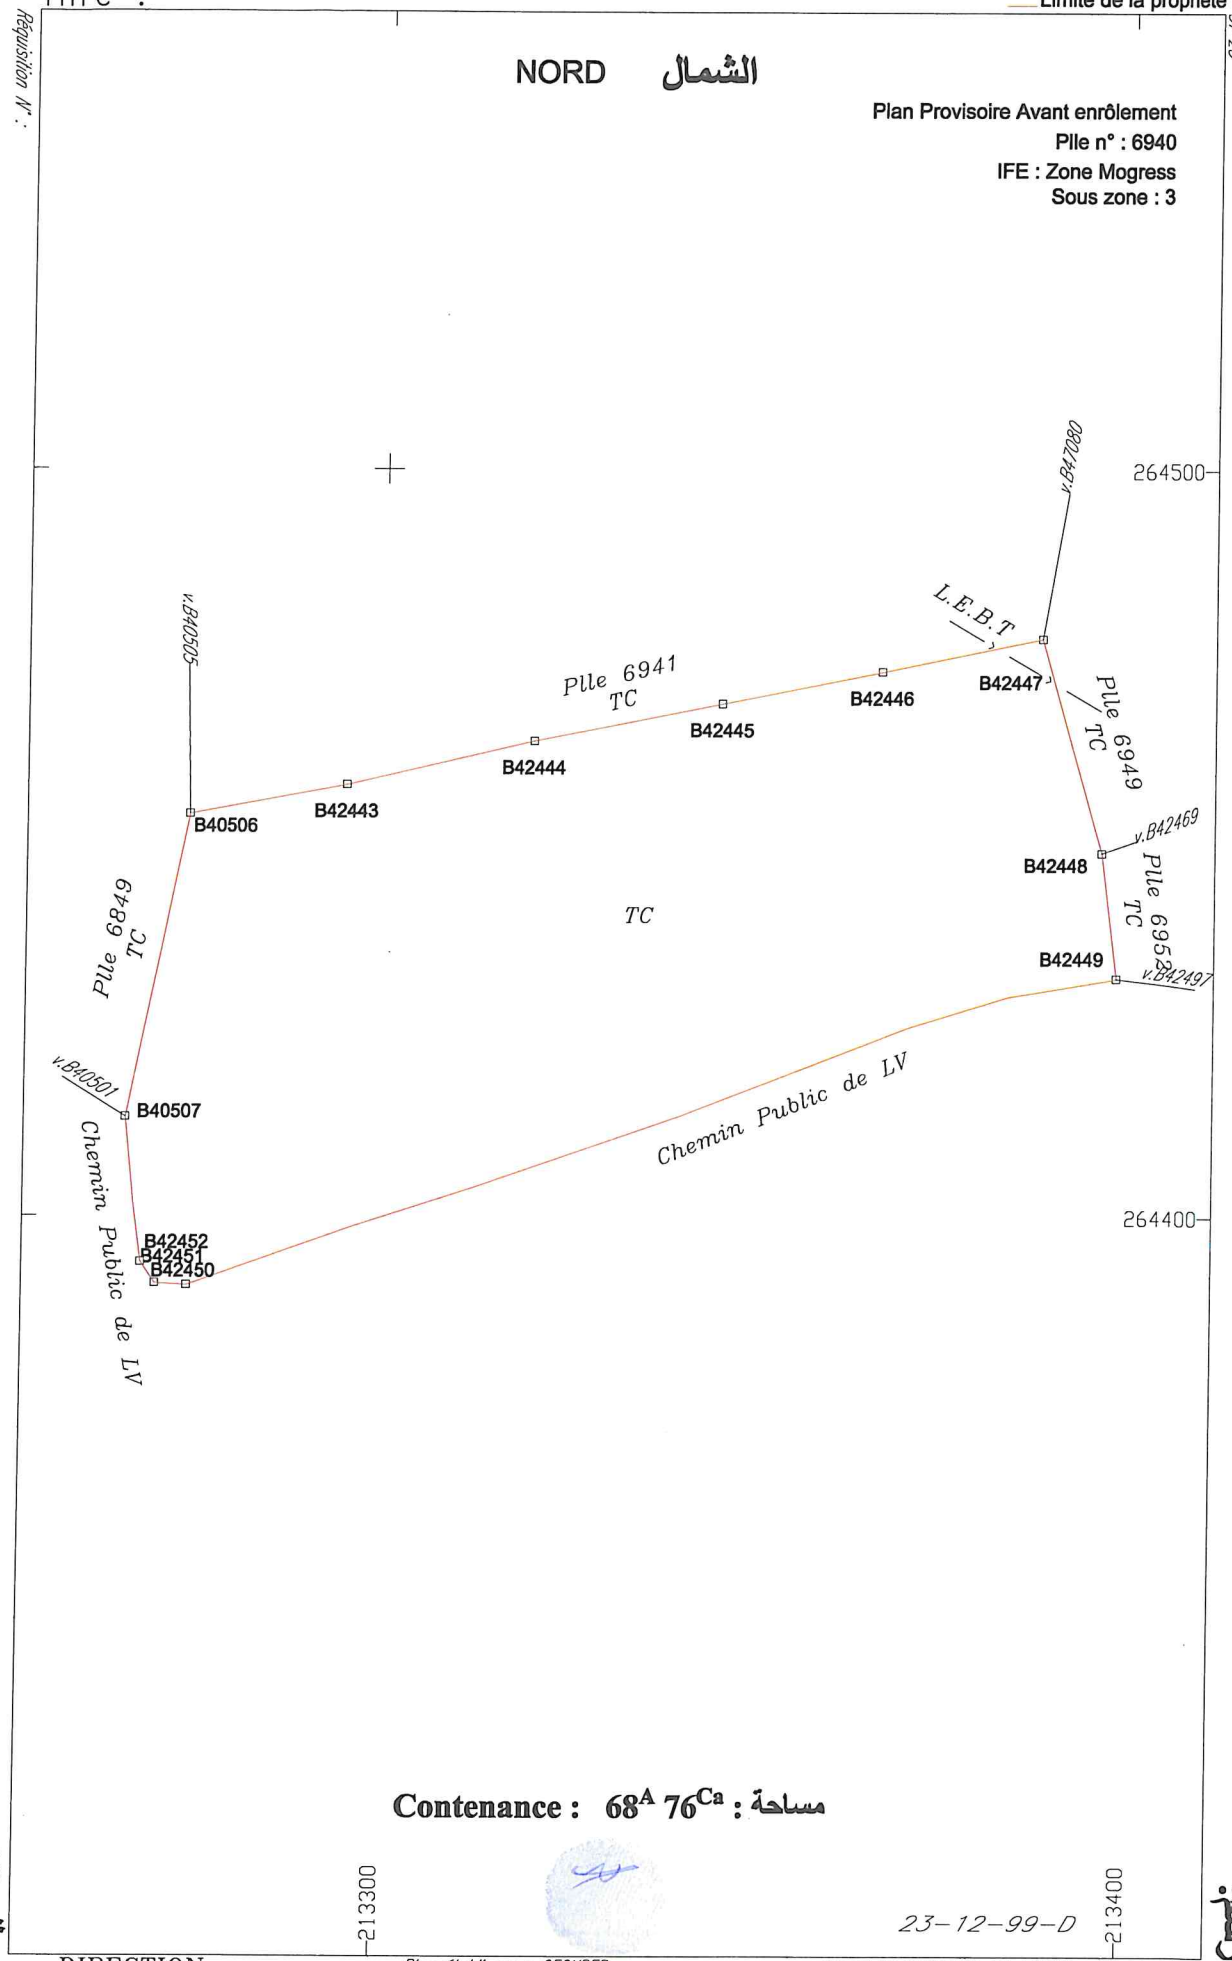

Contenance : $68^{A}\ 76^{Ca}$: مساحة

23-12-99-D

DIRECTION DU CADASTRE

Plan établi par : GEOXPER
Géomètre : MJOUEL Mohamed Amjad
Dessinateur : Automatique

MAPPE DE REPERAGE AU 1/2000 : 23-12-99
CARTE TOPOGRAPHIQUE DE SOUK ARBAA MOGRESS au 1/50000

مطلب عدد:

الملك المسمى :ارض الحفرة

الكائن ب :اقليم الجديدة دائرة سيدي اسماعيل جماعة مكرس دوار الحريشات

رسم:

Propriété dite : Ard Teres


Située à : Pce d'EL JADIDA, Cle de SIDI SMAIL, Cne. Mogress, Dr LAHRICHATE

Titre :

Echelle : 1/500

Plan levé en : Mai 2025

Limite de la propriété

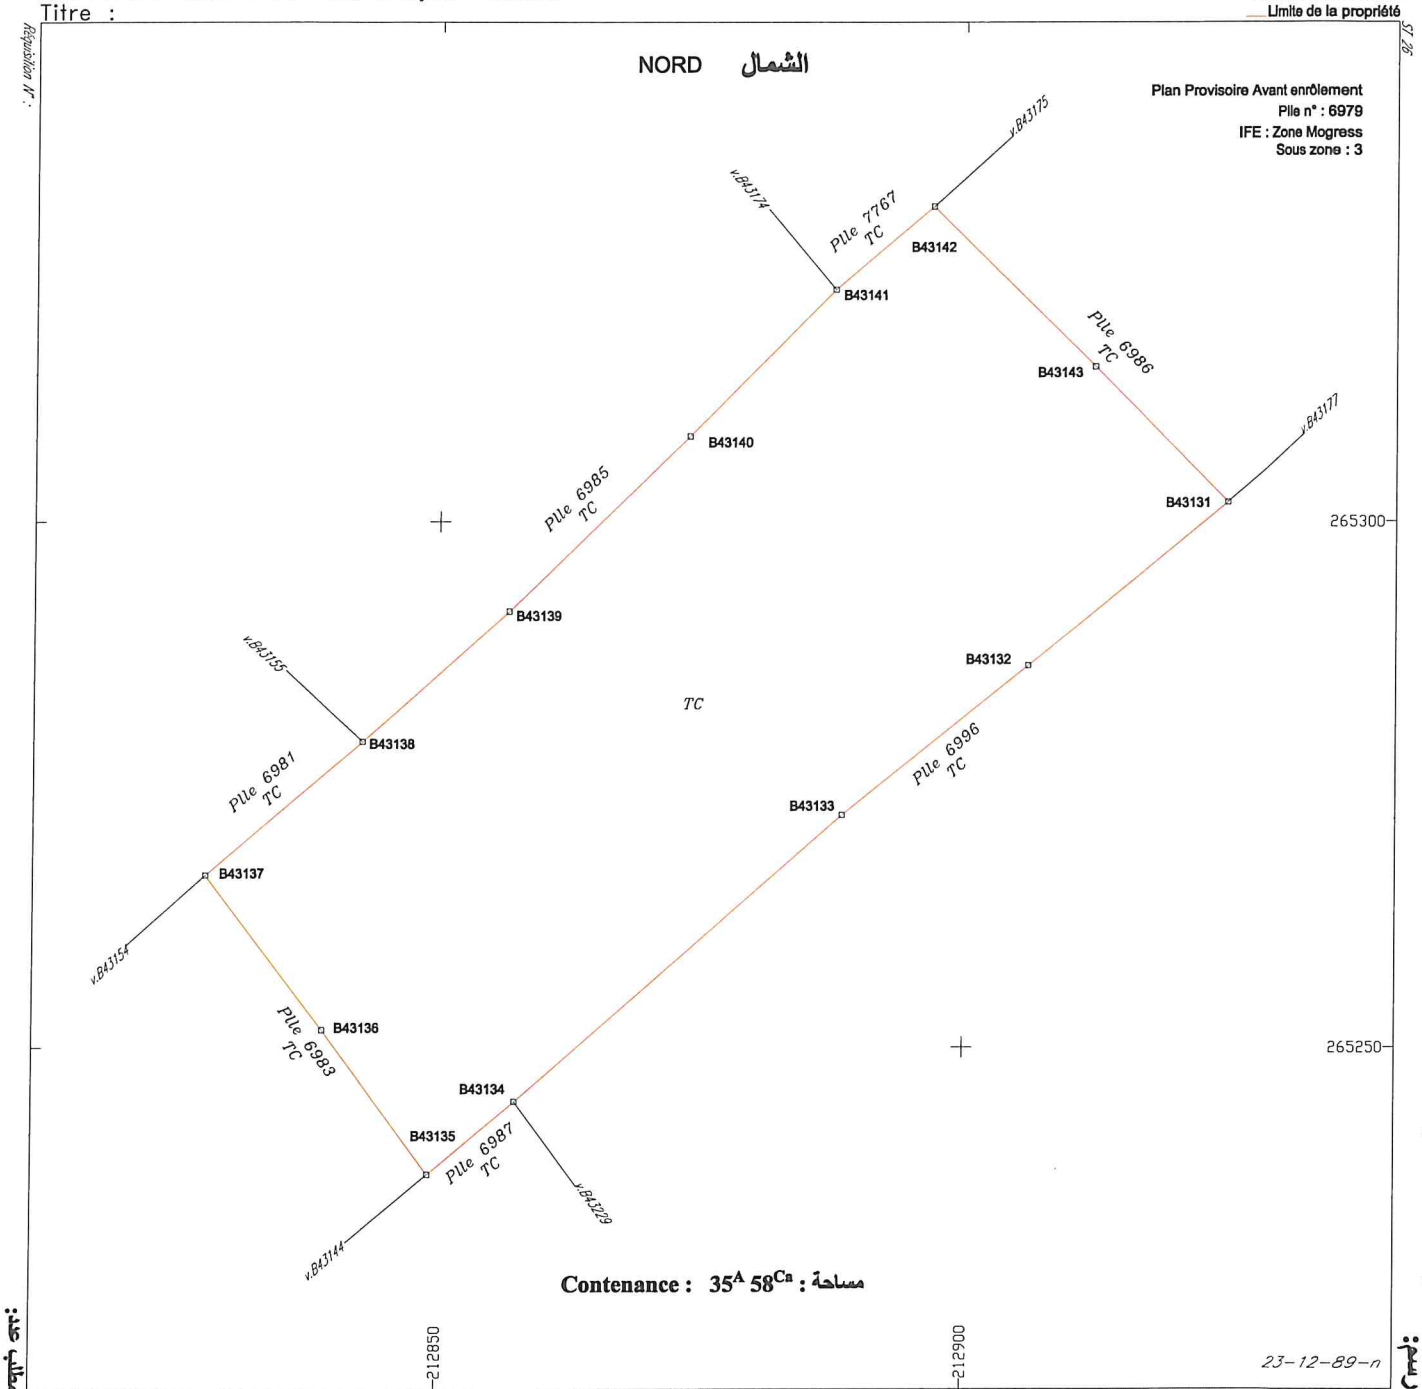

الملك المسمى :ارض تيرس

الكائن ب :إقليم الجديدة دائرة سيدي اسماعيل جماعة مكرس دوار الحريشات

رسم:

مطلب عدد:

DIRECTION
DU CADASTRE

Plan établi par : GEOXPER
Géomètre : MJOUEL Mohamed Amjod
Dessinateur : Automatique

MAPPE DE REPERAGE AU 1/2000 : 23-12-89
CARTE TOPOGRAPHIQUE DE SOUK ARBAA MOGRESS au 1/50000

Propriété dite : Ard El Hamri

Située à : Pce d'EL JADIDA, Cle de SIDI SMAIL, Cne. Mogress, Dr LAHRICHATE

Titre :

Echelle : 1/1000

Plan levé en : Mai 2025

Limite de la propriété

Réquisition N° :

St 25

NORD الشمال

Plan Provisoire Avant enrôlement

Plle n° : 6857

IFE : Zone Mogress

Sous zone : 3

v.B42699

B40566

B40567

B40568

Plle 6968 TC

B40569

B40570

B40571

v.B42704

Bouchaib Dounoune TC

B42705

B40572

B40573

v.B42688

B40574

Plle 6965 TC

B40575

TC

Piste Publique de 10 m

B40577

B40576

Plle 6964 TC

v.B42684

B40578

B40579

v.B42683

Plle 6963 TC

v.B43885

264500

264400

264300

212900

Contenance : 53A 47Ca : مساحة

23-12-99-C

DIRECTION DU CADASTRE

Plan établi par : GEOXPER

Géomètre : MJOUEL Mohamed Amjad

Dessinateur : Automatique

MAPPE DE REPERAGE AU 1/2000 : 23-12-99

CARTE TOPOGRAPHIQUE DE SOUK ARBAA MOGRESS au 1/50000

الملك المسمى :ارض الحمري

الكائن ب :اقليم الجديدة دائرة سيدي اسماعيل جماعة مكرس دوار الحريشات

رسم :

مطلب عدد:

Propriété dite : Ard Remel


Située à : Pce d'EL JADIDA, Ce de SIDI SMAIL, Cne. Mogress, Dr LAHRICHATE

Titre :

Echelle : 1/500

Plan levé en : Mai 2025

Limite de la propriété

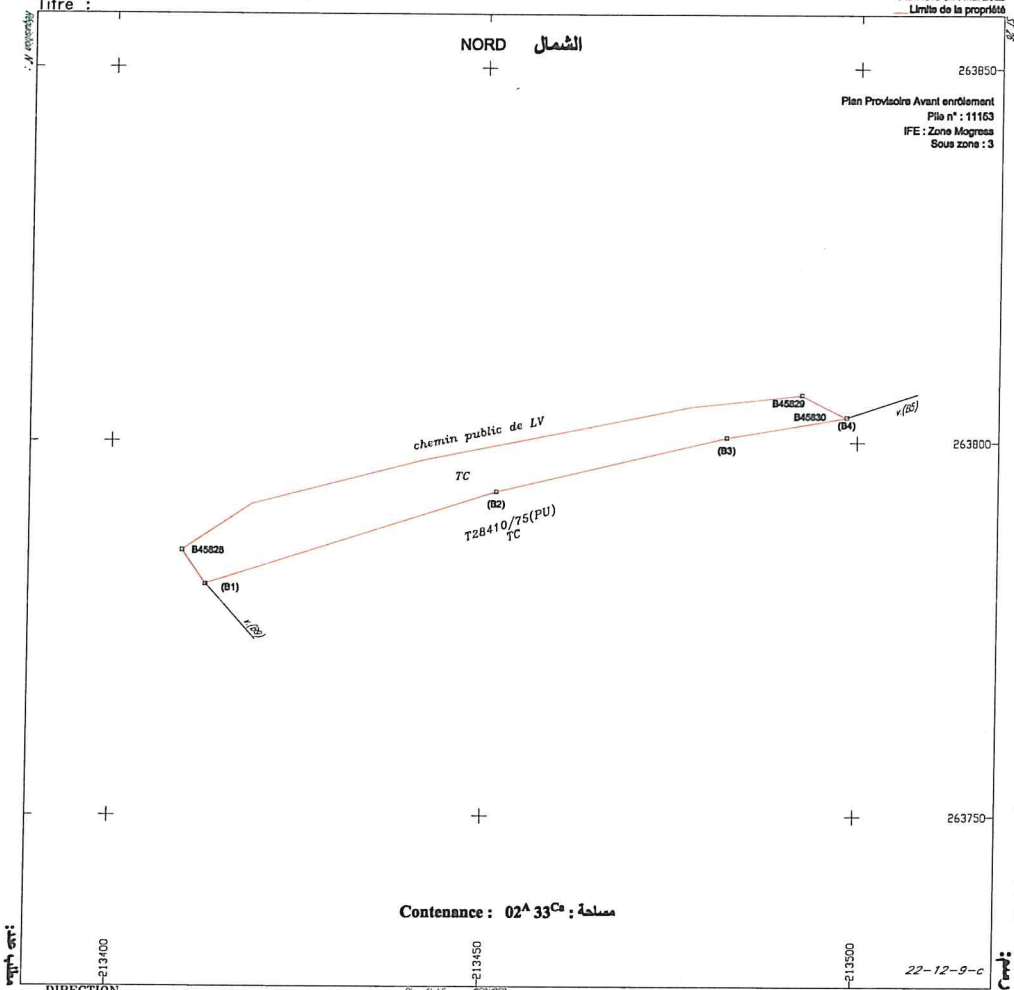

Contenance : 02^A 33^Ca : مساحة

22-12-9-c

DIRECTION
DU CADASTRE

Plan établi par : QGIS/PER
Géomètre : MOUEL Mohamed Amjad
Dessinateur : Automatique

MAPPE DE REFERANCE AU 1/2000 : 22-12-9
CARTE TOPOGRAPHIQUE DE SOUK ARBAA MOGRESS au 1/50000

المالك المسمى : ارض رمل

المكون ب : بالقيم الجديدة ناثرة سيدي اسماعيل جماعة مكرس دوار الحريشات

رسم :

مطلب عدد :

Propriété dite : Ard Remel

Située à : Pce d'EL JADIDA, Cle de SIDI SMAIL, Cne. Mogress, Dr LAHRICHATE

Titre :

Echelle : 1/2000

Plan levé en : Mai 2025

Limite de la propriété

Réquisition N° :


NORD الشمال

Plan Provisoire Avant enrôlement

Plle n° : 11154

IFE : Zone Mogress

Sous zone : 3

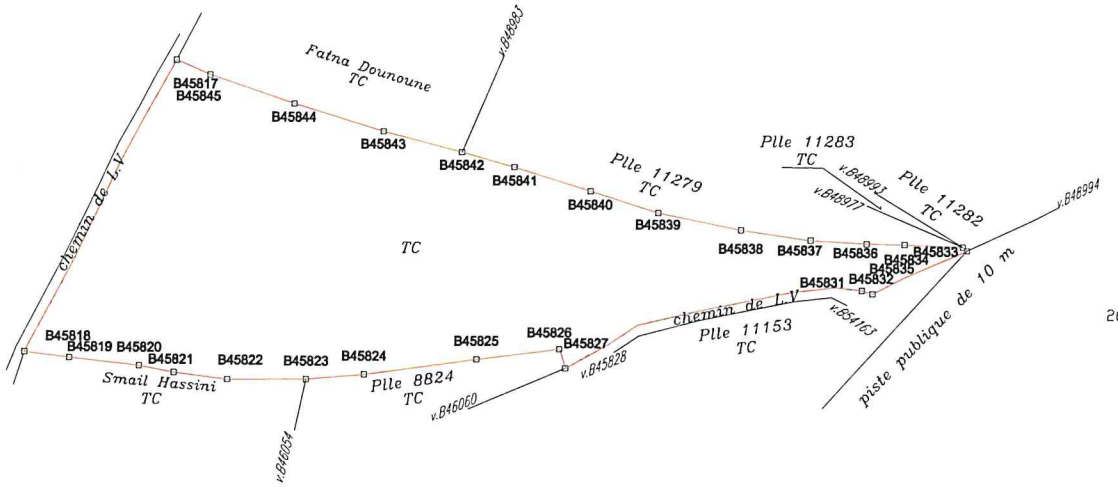

Contenance : $02^{Ha}\ 16^{A}\ 87^{Ca}$: مساحة

264000

263800

263600

213200

213400

213600

22-12-9

الملك المسمى :ارض رمل

الكائن ب :إقليم الجديدة دائرة سيدي اسماعيل جماعة مكرس دوار الحريشات

رسم :

مطلب عدد :

DIRECTION
DU CADASTRE

Plan Etabli par : GEOXPER
Géomètre : MJOUEL Mohamed Anjod
Dessinateur : Automatique

MAPPE DE REPERAGE AU 1/2000 : 22-12-9
CARTE TOPOGRAPHIQUE DE SOUK ARBAA MOGRESS au 1/50000