# Propriété dite : Ard El Hofra

*Située à : Pce d'EL JADIDA, Cle de SIDI SMAIL, Cne. Mogress, Dr LAHRICHATE*

Titre :

**Echelle : 1/1000**

**Plan levé en : Mai 2025**

Limite de la propriété

Réquisition N° :

ST 25


**NORD الشمال**

**Plan Provisoire Avant enrôlement**

**Plle n° : 6940**

**IFE : Zone Mogress**

**Sous zone : 3**

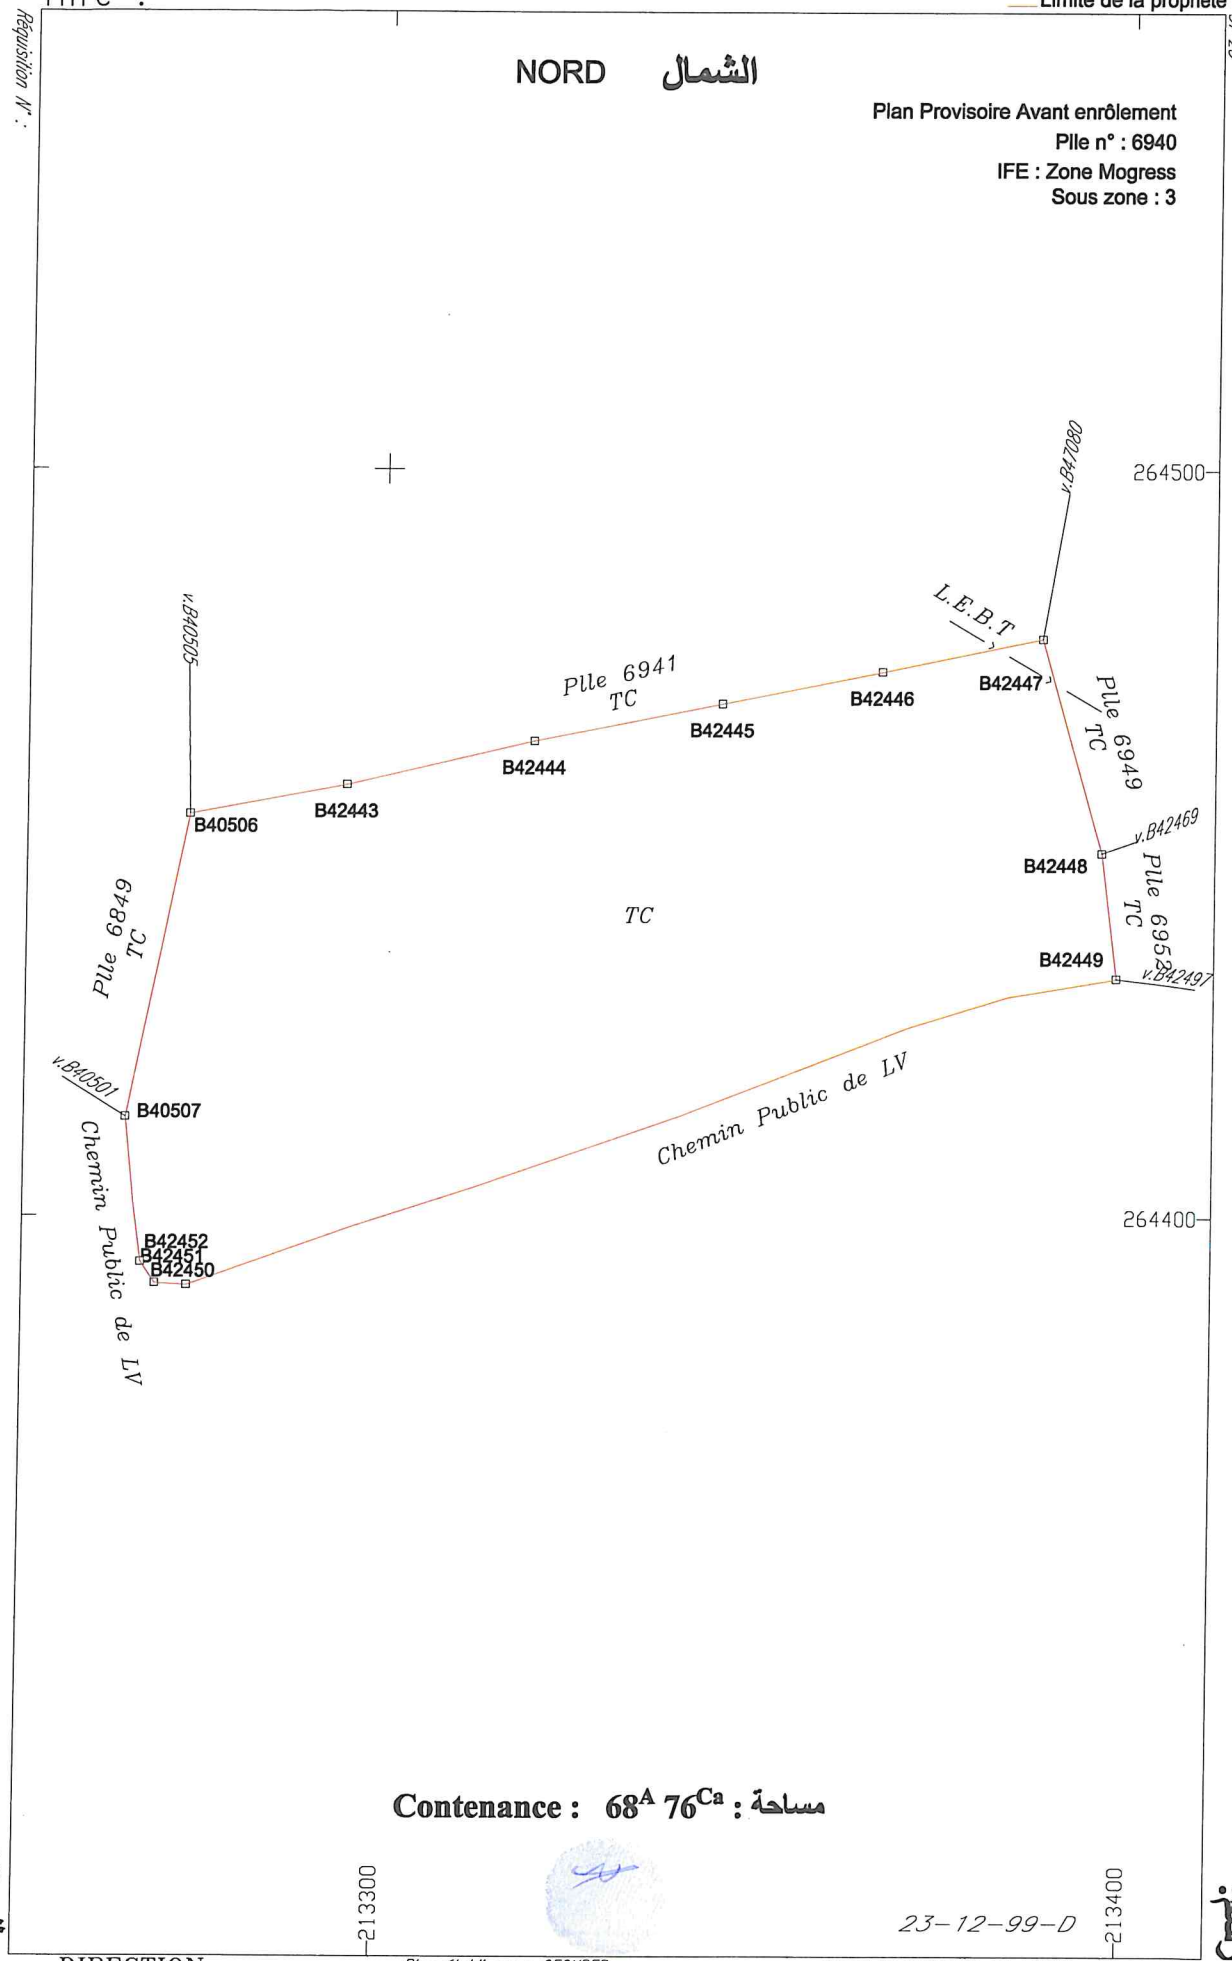


**Contenance : $68^{A}\ 76^{Ca}$ : مساحة**

23-12-99-D

DIRECTION DU CADASTRE

*Plan établi par : GEOXPER*
*Géomètre : MJOUEL Mohamed Amjad*
*Dessinateur : Automatique*

*MAPPE DE REPERAGE AU 1/2000 : 23-12-99*
*CARTE TOPOGRAPHIQUE DE SOUK ARBAA MOGRESS au 1/50000*

مطلب عدد:

**الملك المسمى :ارض الحفرة**

**الكائن ب :اقليم الجديدة دائرة سيدي اسماعيل جماعة مكرس دوار الحريشات**

رسم:

# Propriété dite : Ard El Hamri

*Située à : Pce d'EL JADIDA, Cle de SIDI SMAIL, Cne. Mogress, Dr LAHRICHATE*

Titre :

**Echelle : 1/1000**

Plan levé en : Mai 2025

Limite de la propriété

Réquisition N° :

St 25

NORD الشمال

Plan Provisoire Avant enrôlement

Plle n° : 6857

IFE : Zone Mogress

Sous zone : 3

v.B42699

B40566

B40567

B40568

Plle 6968 TC

B40569

B40570

B40571

v.B42704

Bouchaib Dounoune TC

B42705

B40572

B40573

v.B42688

B40574

Plle 6965 TC

B40575

TC

Piste Publique de 10 m

B40577

B40576

Plle 6964 TC

v.B42684

B40578

B40579

v.B42683

Plle 6963 TC

v.B43885

264500

264400

264300

212900

**Contenance : 53A 47Ca : مساحة**

23-12-99-C

DIRECTION DU CADASTRE

*Plan établi par : GEOXPER*

*Géomètre : MJOUEL Mohamed Amjad*

*Dessinateur : Automatique*

*MAPPE DE REPERAGE AU 1/2000 : 23-12-99*

*CARTE TOPOGRAPHIQUE DE SOUK ARBAA MOGRESS au 1/50000*

**الملك المسمى :ارض الحمري**

**الكائن ب :اقليم الجديدة دائرة سيدي اسماعيل جماعة مكرس دوار الحريشات**

**رسم :**

**مطلب عدد:**