الموافقة على عملية التحديد

انا الموقع اسفله **عبد الفتاح شفيق بن مبارك** الحامل(ة) للبطاقة الوطنية رقم **M211522**

والساكن(ة)ب : **دوار الهيالمة المهارزة الساحل البئر الجديد** .


أصرح اطلاعي على المعطيات الهندسية الناتجة عن عملية البحث التجزيئي(التصميم، الصورة الجوية، الحدود، المجاورون، المساحة، المشتملات) المتعلقة بالقطعة رقم **11039** الكائنة بدوار **الحريشات**.

قيادة سيدي إسماعيل دائرة سيدي إسماعيل إقليم الجديدة منطقة التحفيظ الجماعي المدعوة مكرس.

انني أوافق على عملية التحديد المزمع إجراؤها بشأن القطعة المعنية اعتمادا على المعطيات الهندسية المشار اليها أعلاه.

حرر ب **دوار الحريشات** بتاريخ:**2025/08/22**

الامضاء و البصمة

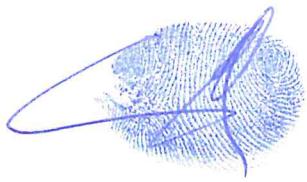


Parcelle N°: 11039

Propriété Dite : Ard El Oued

I.F.E Mogress
Sous_Zone 3

Echelle Appx-1/500

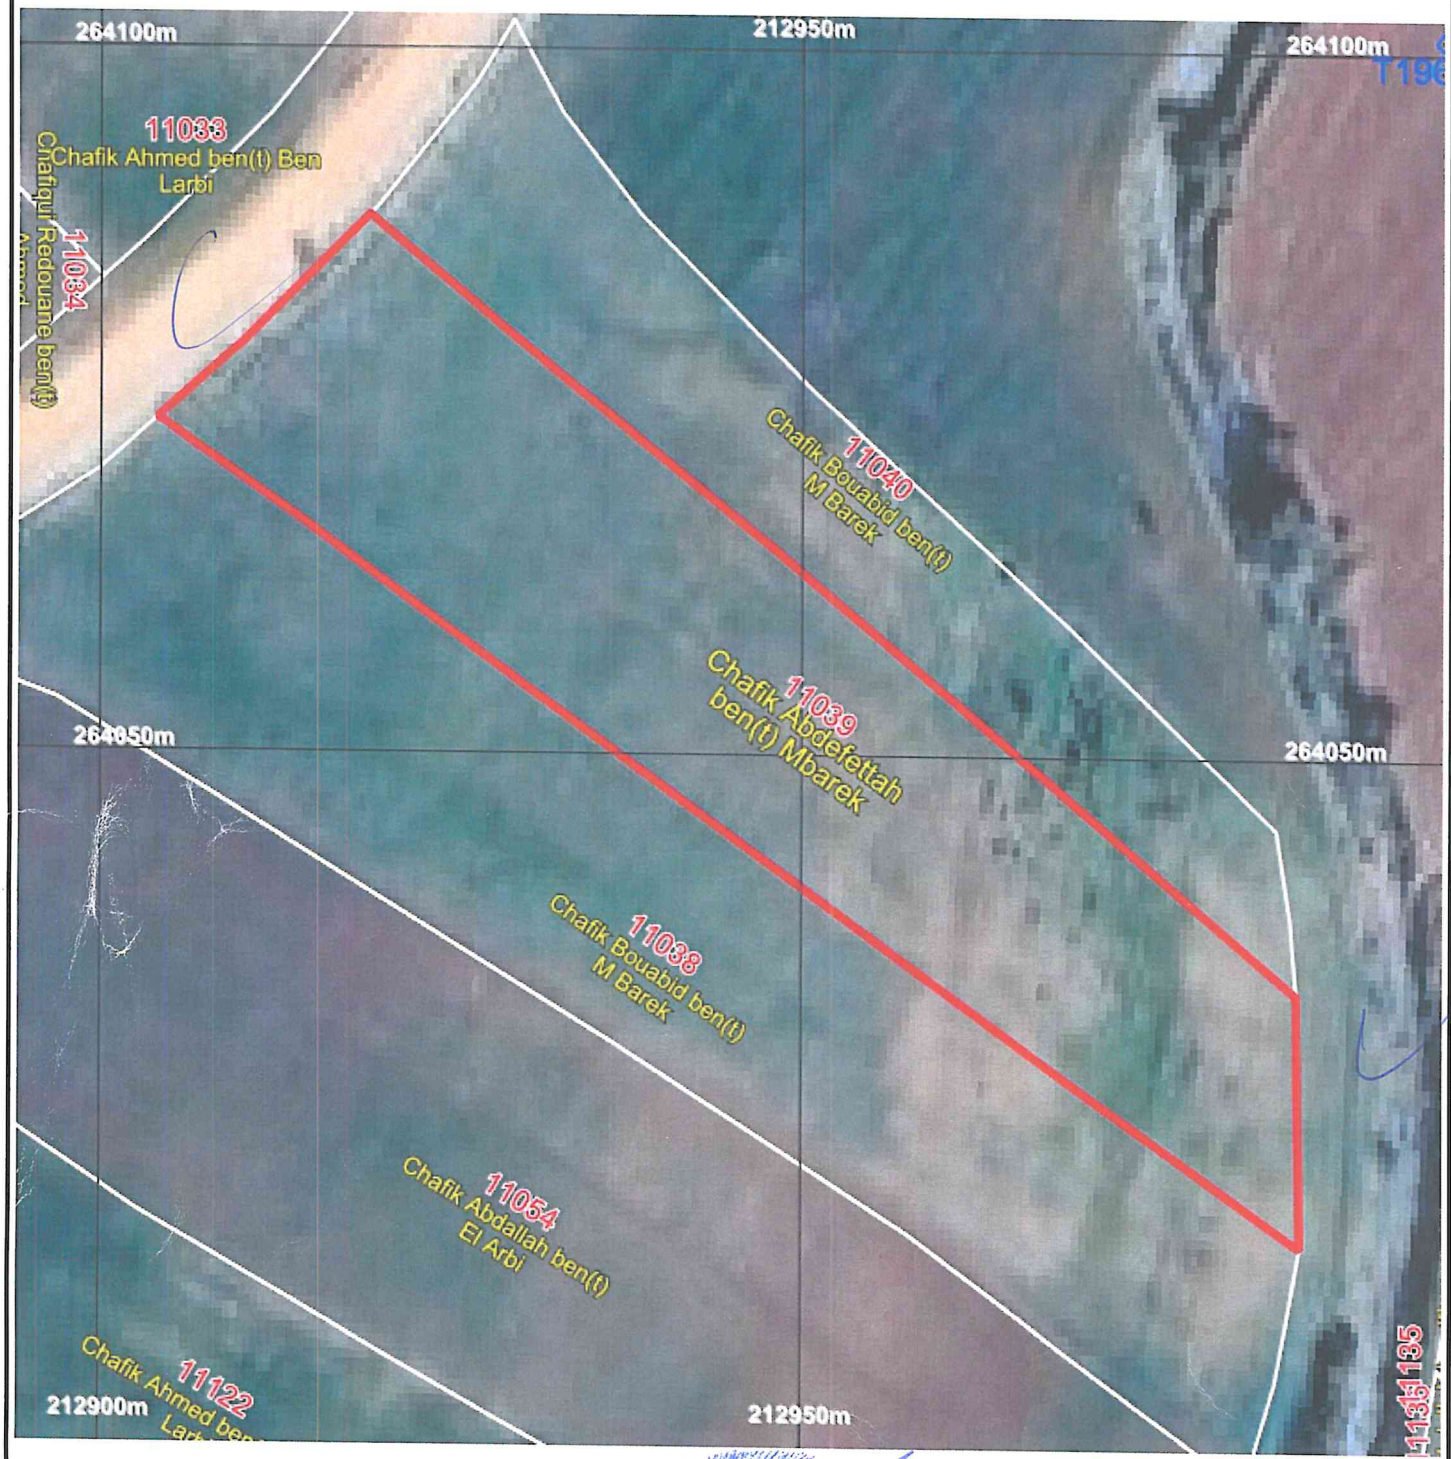

Mappe(1/2000)
23-12-99

Propriété dite : Ard El Oued

Située à : Pce d'EL JADIDA, Cle de SIDI SMAIL, Cne. Mogress, Dr LAHRICHATE

Titre :

Echelle : 1/500

Plan levé en : Mai 2025

Limite de la propriété

Réquisition N° :

ST 26

NORD الشمال

Plan Provisoire Avant enrôlement
Plle n° : 11039
IFE : Zone Mogress
Sous zone : 3

264100

piste publique de 10 m

v.B43812

B43822

B43823

Plle 11040
TC

B43821

v.B43809

B43820

B43824

TC

B43819

Plle 11038
TC

B43825

B43818

v.B43827

B43826

B43817

oued

B43816

v.B43815

264050

264000

Contenance : $16^{A}\ 31^{Ca}$: مساحة

212900

212950

213000

23-12-99-n

DIRECTION
DU CADASTRE

Plan établi par : GEOXPER
Géomètre : MJOUEL Mohamed Amjad
Dessinateur : Automatique

MAPPE DE REPERAGE AU 1/2000 : 23-12-99
CARTE TOPOGRAPHIQUE DE SOUK ARBAA MOGRESS au 1/50000

مطلب عدد:

الملك المسمى :ارض الواد

الكائن ب :إقليم الجديدة دائرة سيدي اسماعيل جماعة مكرس دوار الحريشات

رسم: