الموافقة على عملية التحديد

انا الموقع **المصطفى دنون بن محمد** الحامل(ة) للبطاقة الوطنية رقم **M184701**

والساكن(ة)ب : **دوار الحريشات مكرس الجديدة** .

أصرح اطلاعي على المعطيات الهندسية الناتجة عن عملية البحث التجزيئي(التصميم، الصورة الجوية، الحدود، المجاورون، المساحة، المشتملات) المتعلقة بالقطعة رقم **11154** الكائنة بدوار **الحريشات**.

قيادة سيدي إسماعيل دائرة سيدي إسماعيل إقليم الجديدة منطقة التحفيظ الجماعي المدعوة مكرس.

انني أوافق على عملية التحديد المزمع إجراؤها بشأن القطعة المعنية اعتمادا على المعطيات الهندسية المشار اليها أعلاه.

حرر ب **دوار الحريشات** بتاريخ:**2025/08/22**

الامضاء و البصمة




Parcelle N°: 11154

Propriété Dite : Ard Remel

I.F.E Mogress
Sous_Zone 3

Echelle Appx-1/2000

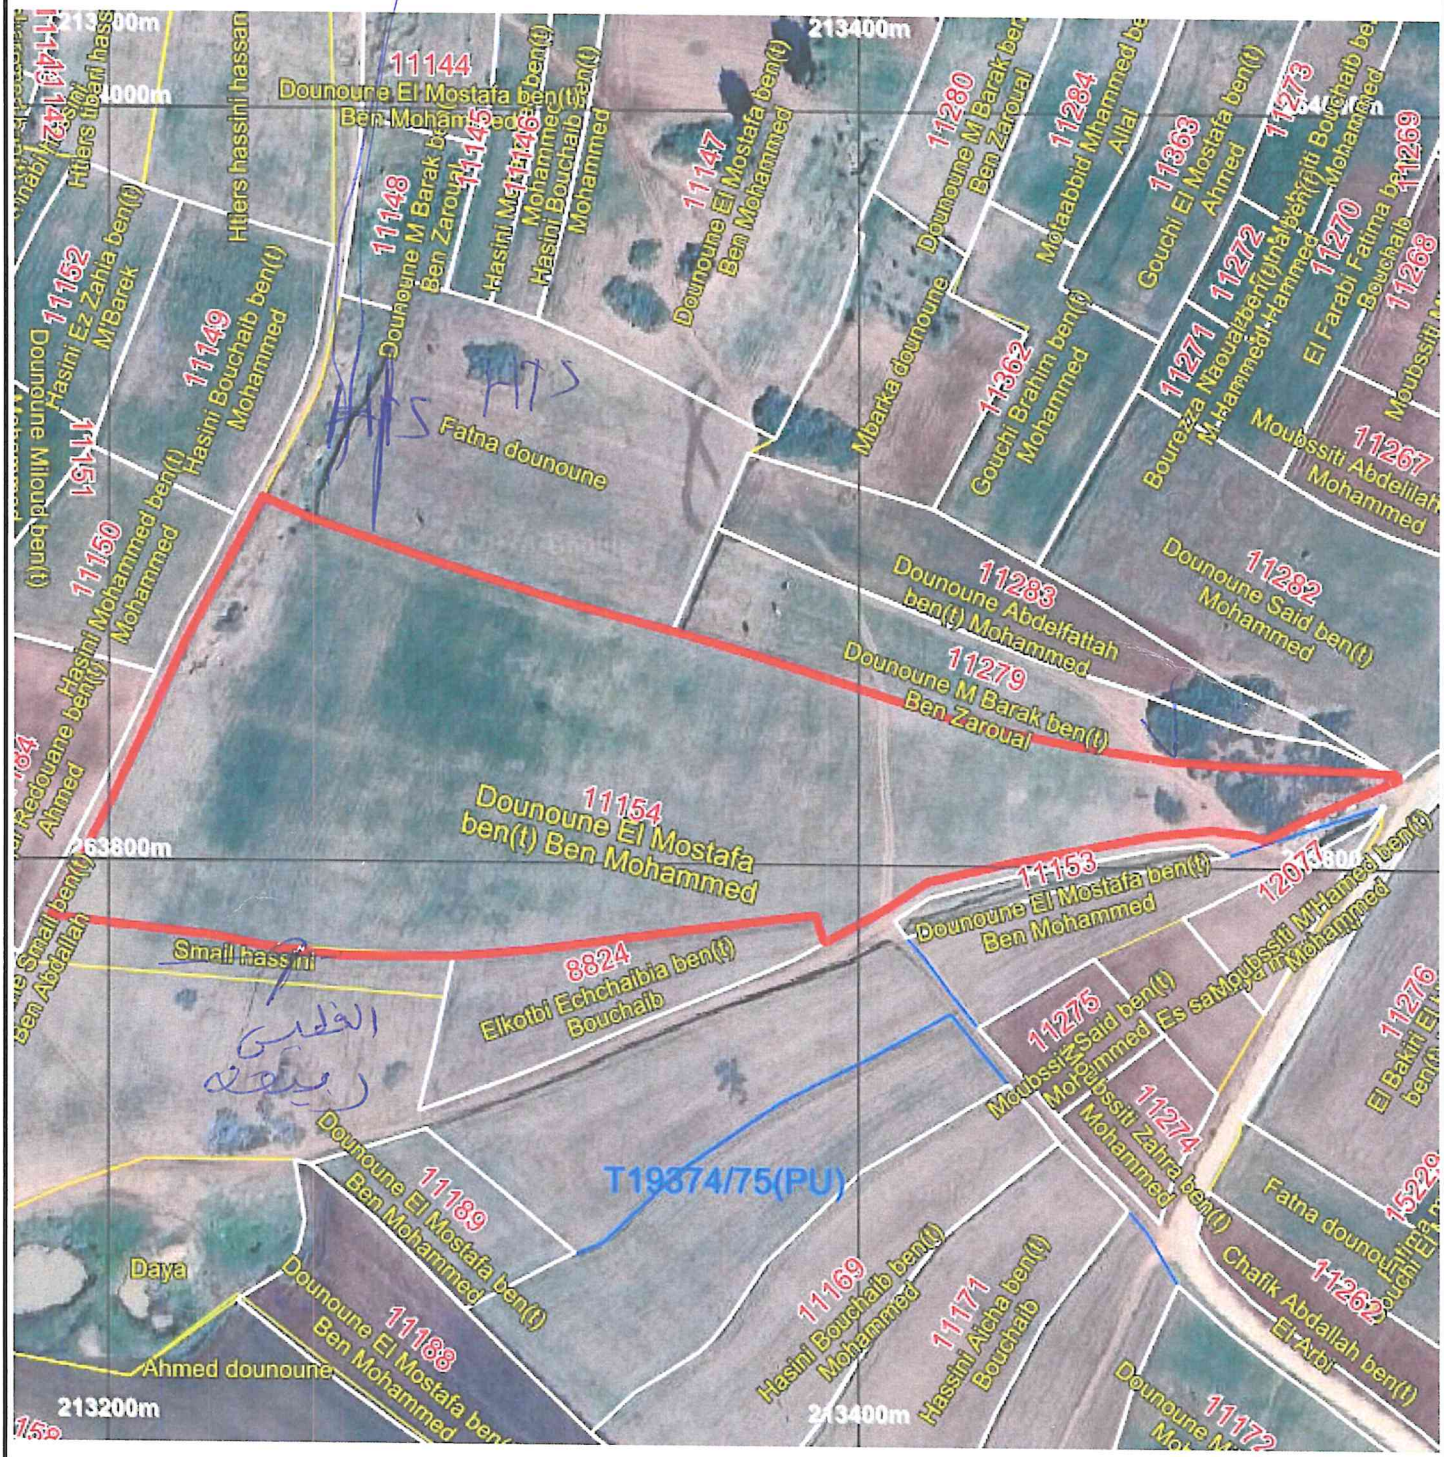

Mappe(1/2000)
22-12-9

Propriété dite : Ard Remel

Située à : Pce d'EL JADIDA, Cle de SIDI SMAIL, Cne. Mogress, Dr LAHRICHATE

Titre :

Echelle : 1/2000

Plan levé en : Mai 2025

Limite de la propriété

Réquisition N° :


NORD الشمال

Plan Provisoire Avant enrôlement

Plle n° : 11154

IFE : Zone Mogress

Sous zone : 3

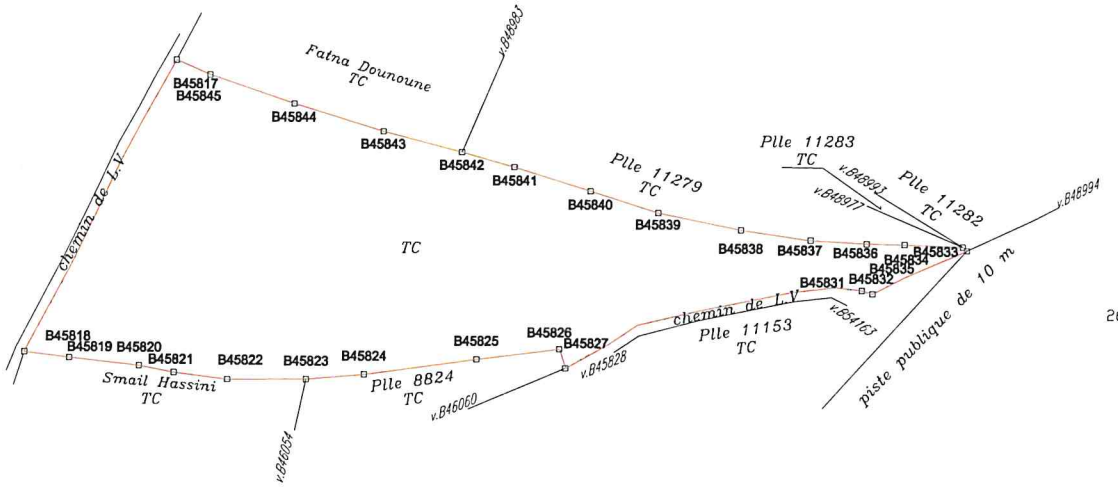

Contenance : $02^{Ha}\ 16^{A}\ 87^{Ca}$: مساحة

264000

263800

263600

213200

213400

213600

22-12-9

الملك المسمى :ارض رمل

الكائن ب :إقليم الجديدة دائرة سيدي اسماعيل جماعة مكرس دوار الحريشات

رسم :

مطلب عدد :

DIRECTION
DU CADASTRE

Plan Etabli par : GEOXPER
Géomètre : MJOUEL Mohamed Anjod
Dessinateur : Automatique

MAPPE DE REPERAGE AU 1/2000 : 22-12-9
CARTE TOPOGRAPHIQUE DE SOUK ARBAA MOGRESS au 1/50000