الموافقة على عملية التحديد

انا الموقع **المصطفى دنون بن محمد** الحامل(ة) للبطاقة الوطنية رقم **M184701**

والساكن(ة)ب : **دوار الحريشات مكرس الجديدة** .

أصرح اطلاعي على المعطيات الهندسية الناتجة عن عملية البحث التجزيئي(التصميم، الصورة الجوية، الحدود، المجاورون، المساحة، المشتملات) المتعلقة بالقطعة رقم **6940** الكائنة بدوار **الحريشات**.

قيادة سيدي إسماعيل دائرة سيدي إسماعيل إقليم الجديدة منطقة التحفيظ الجماعي المدعوة مكرس.

انني أوافق على عملية التحديد المزمع إجراؤها بشأن القطعة المعنية اعتمادا على المعطيات الهندسية المشار اليها أعلاه.

حرر ب **دوار الحريشات** بتاريخ:**2025/08/22**

الامضاء و البصمة




Parcelle N°: 6940

Propriété Dite : Ard El Hofra

I.F.E Mogress
Sous_Zone 3

Echelle Appx-1/1000

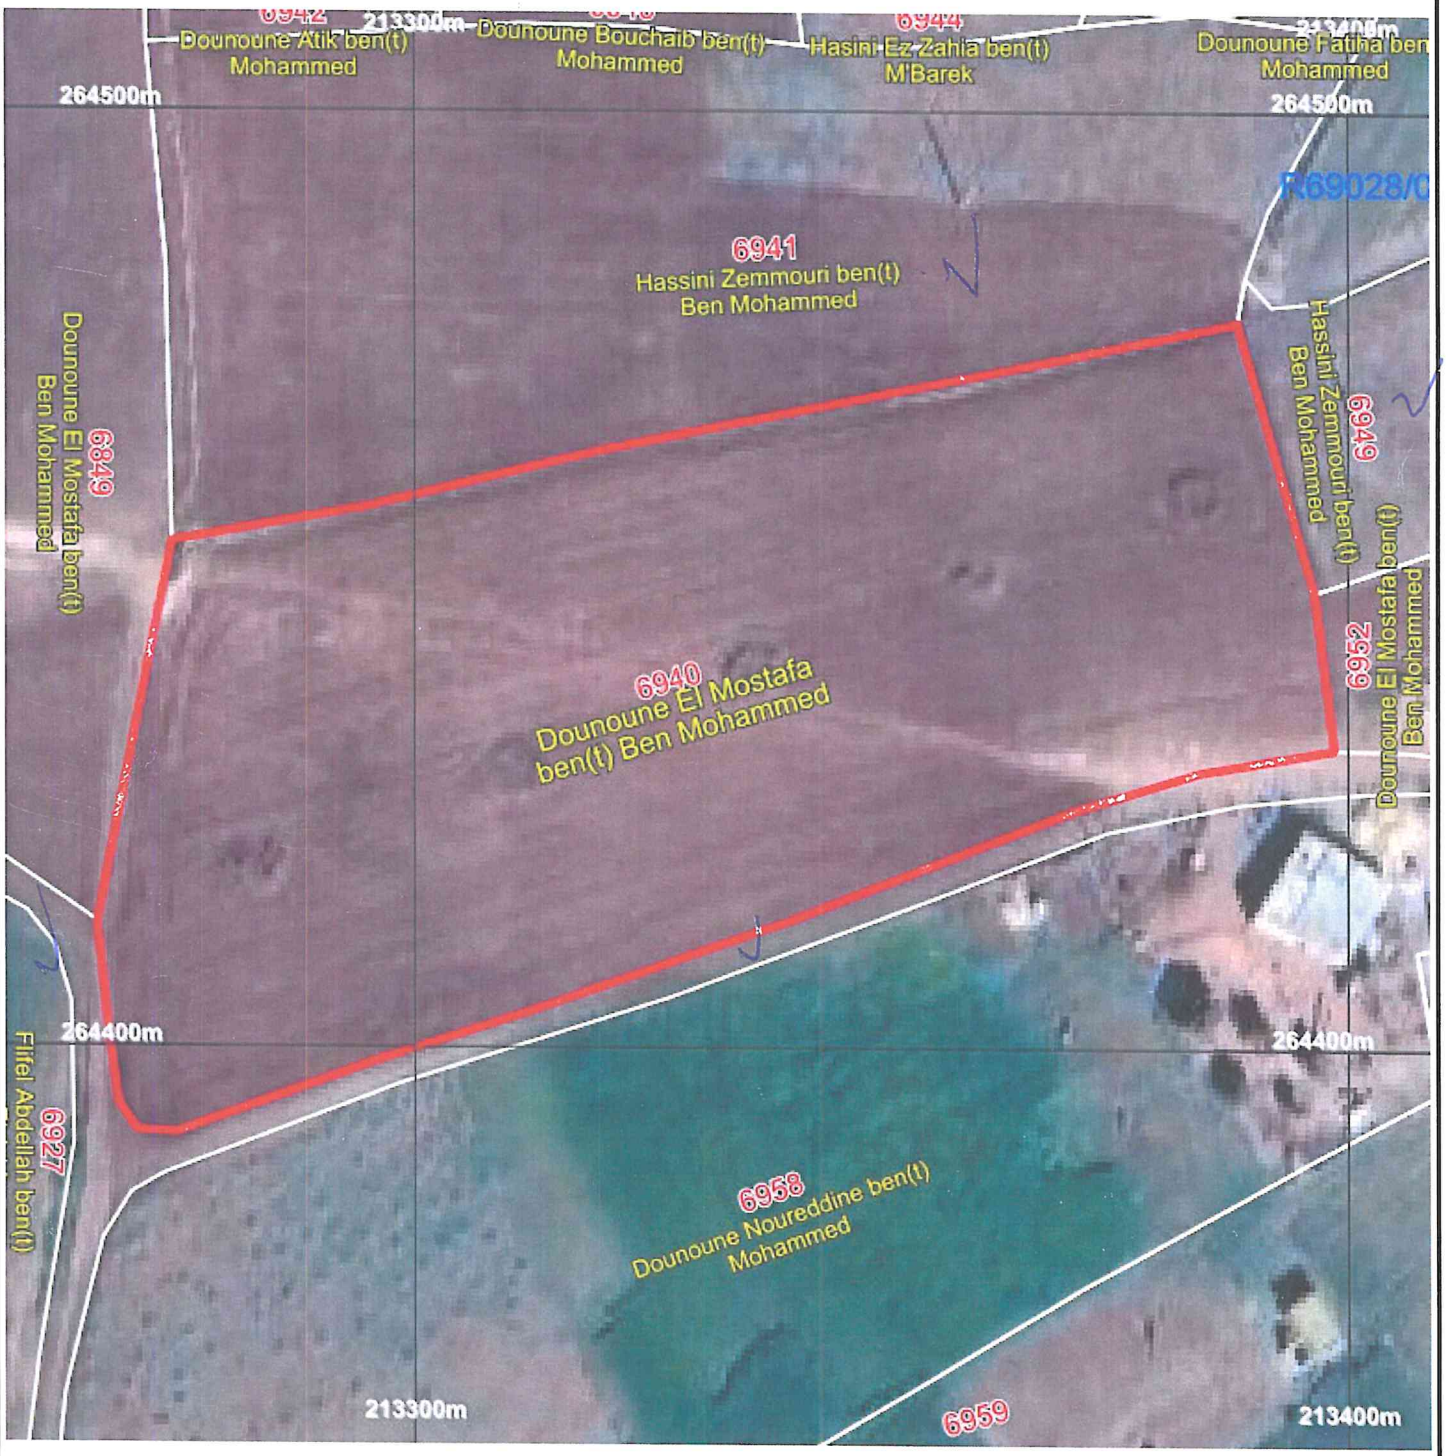

Mappe(1/2000)
23-12-99

Propriété dite : Ard El Hofra

Située à : Pce d'EL JADIDA, Cle de SIDI SMAIL, Cne. Mogress, Dr LAHRICHATE

Titre :

Echelle : 1/1000

Plan levé en : Mai 2025

Limite de la propriété

Réquisition N° :

ST 25


NORD الشمال

Plan Provisoire Avant enrôlement

Plle n° : 6940

IFE : Zone Mogress

Sous zone : 3

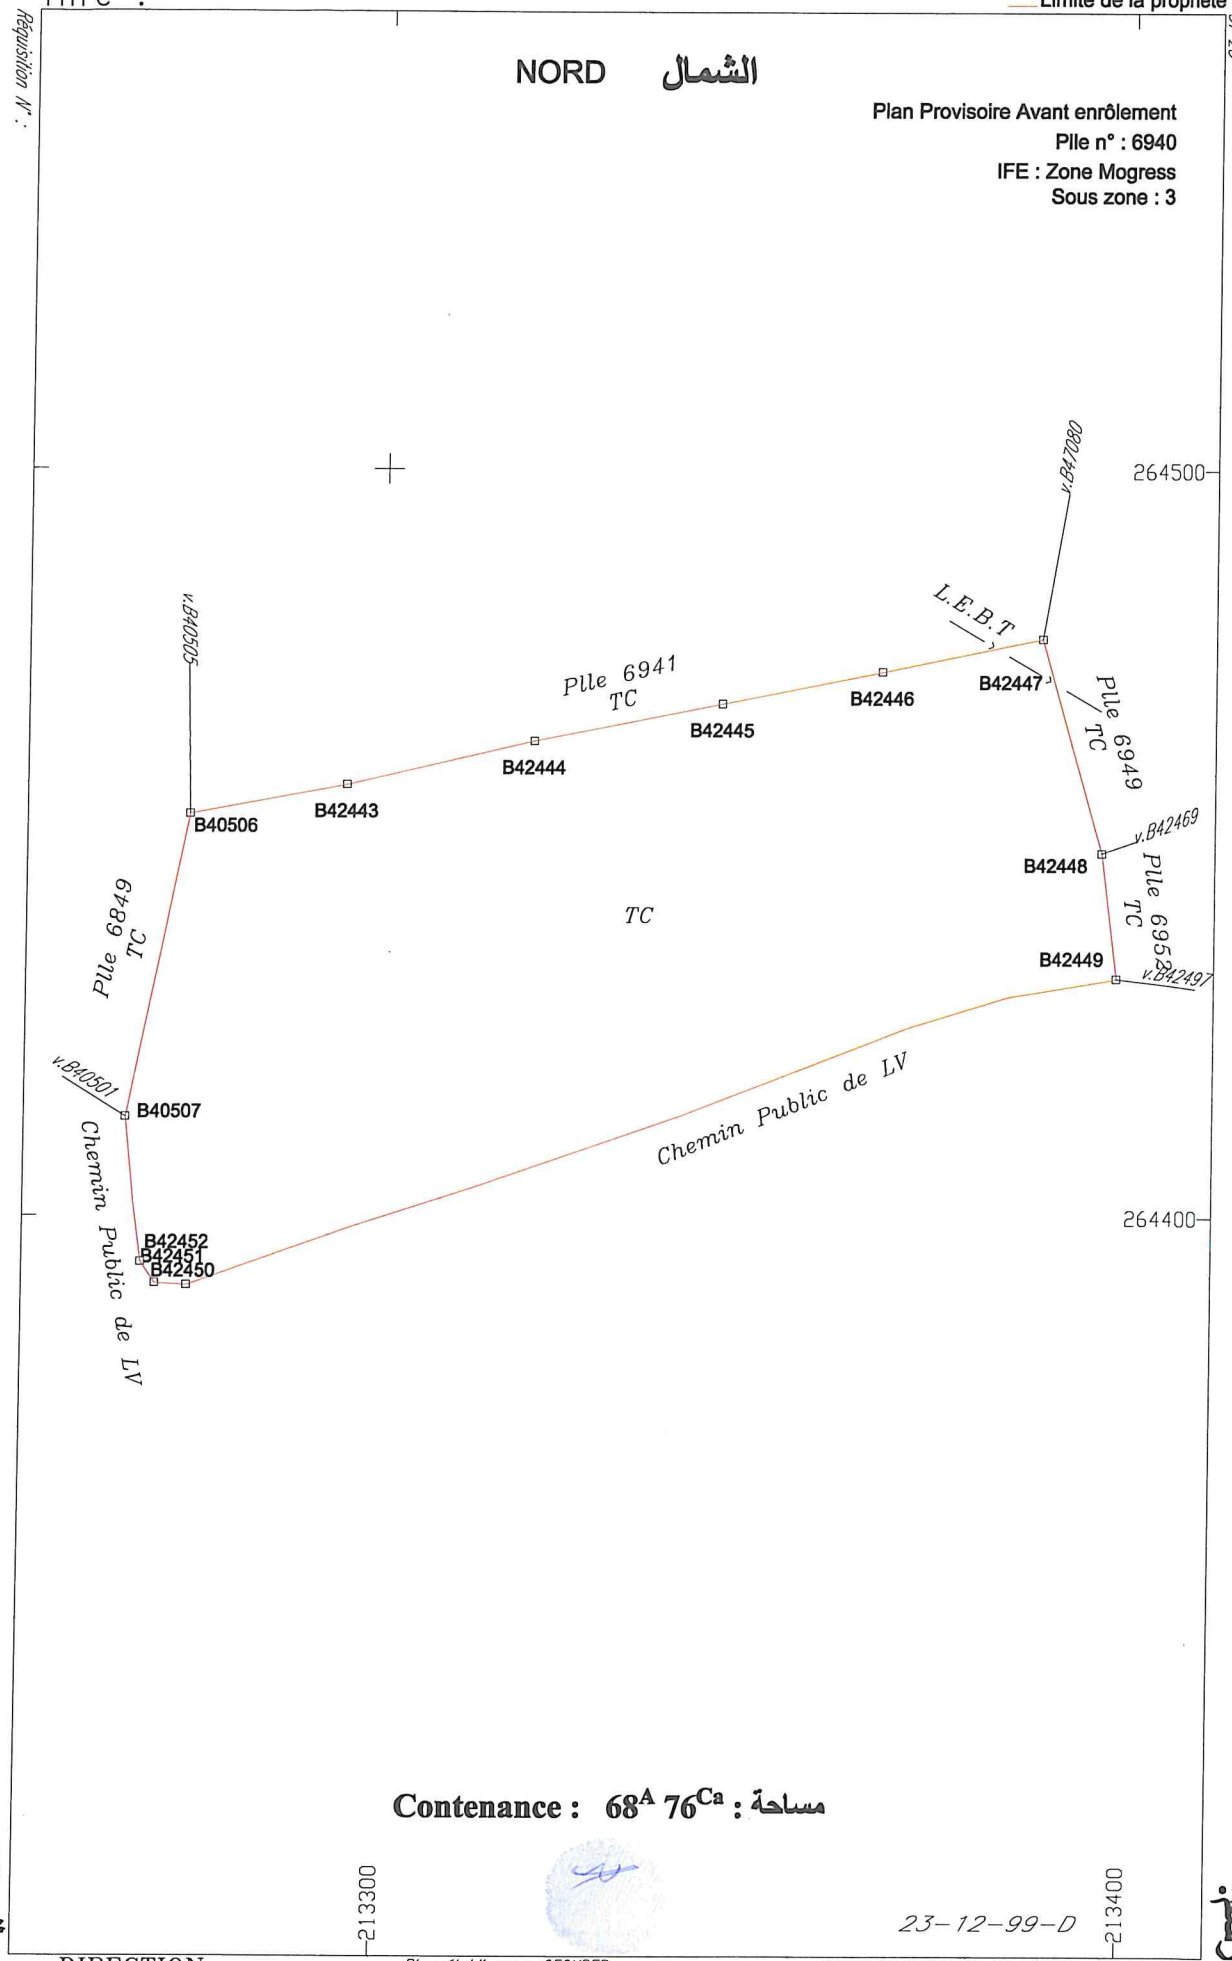

Contenance : $68^{A}\ 76^{Ca}$: مساحة

23-12-99-D

DIRECTION DU CADASTRE

Plan établi par : GEOXPER
Géomètre : MJOUEL Mohamed Amjad
Dessinateur : Automatique

MAPPE DE REPERAGE AU 1/2000 : 23-12-99
CARTE TOPOGRAPHIQUE DE SOUK ARBAA MOGRESS au 1/50000

مطلب عدد:

الملك المسمى :ارض الحفرة

الكائن ب :اقليم الجديدة دائرة سيدي اسماعيل جماعة مكرس دوار الحريشات

رسم: