الموافقة على عملية التحديد

انا الموقع **المصطفى دنون بن محمد** الحامل(ة) للبطاقة الوطنية رقم **M184701**

والساكن(ة)ب : **دوار الحريشات مكرس الجديدة** .

أصرح اطلاعي على المعطيات الهندسية الناتجة عن عملية البحث التجزيئي(التصميم، الصورة الجوية، الحدود، المجاورون، المساحة، المشتملات) المتعلقة بالقطعة رقم **6993** الكائنة بدوار **الحريشات**.

قيادة سيدي إسماعيل دائرة سيدي إسماعيل إقليم الجديدة منطقة التحفيظ الجماعي المدعوة مكرس.

انني أوافق على عملية التحديد المزمع إجراؤها بشأن القطعة المعنية اعتمادا على المعطيات الهندسية المشار اليها أعلاه.

حرر ب **دوار الحريشات** بتاريخ:**2025/08/22**


الامضاء و البصمة

Parcelle N°: 6993

Propriété Dite : Ard Tres

I.F.E Mogress
Sous_Zone 3

Echelle Appx-1/1000

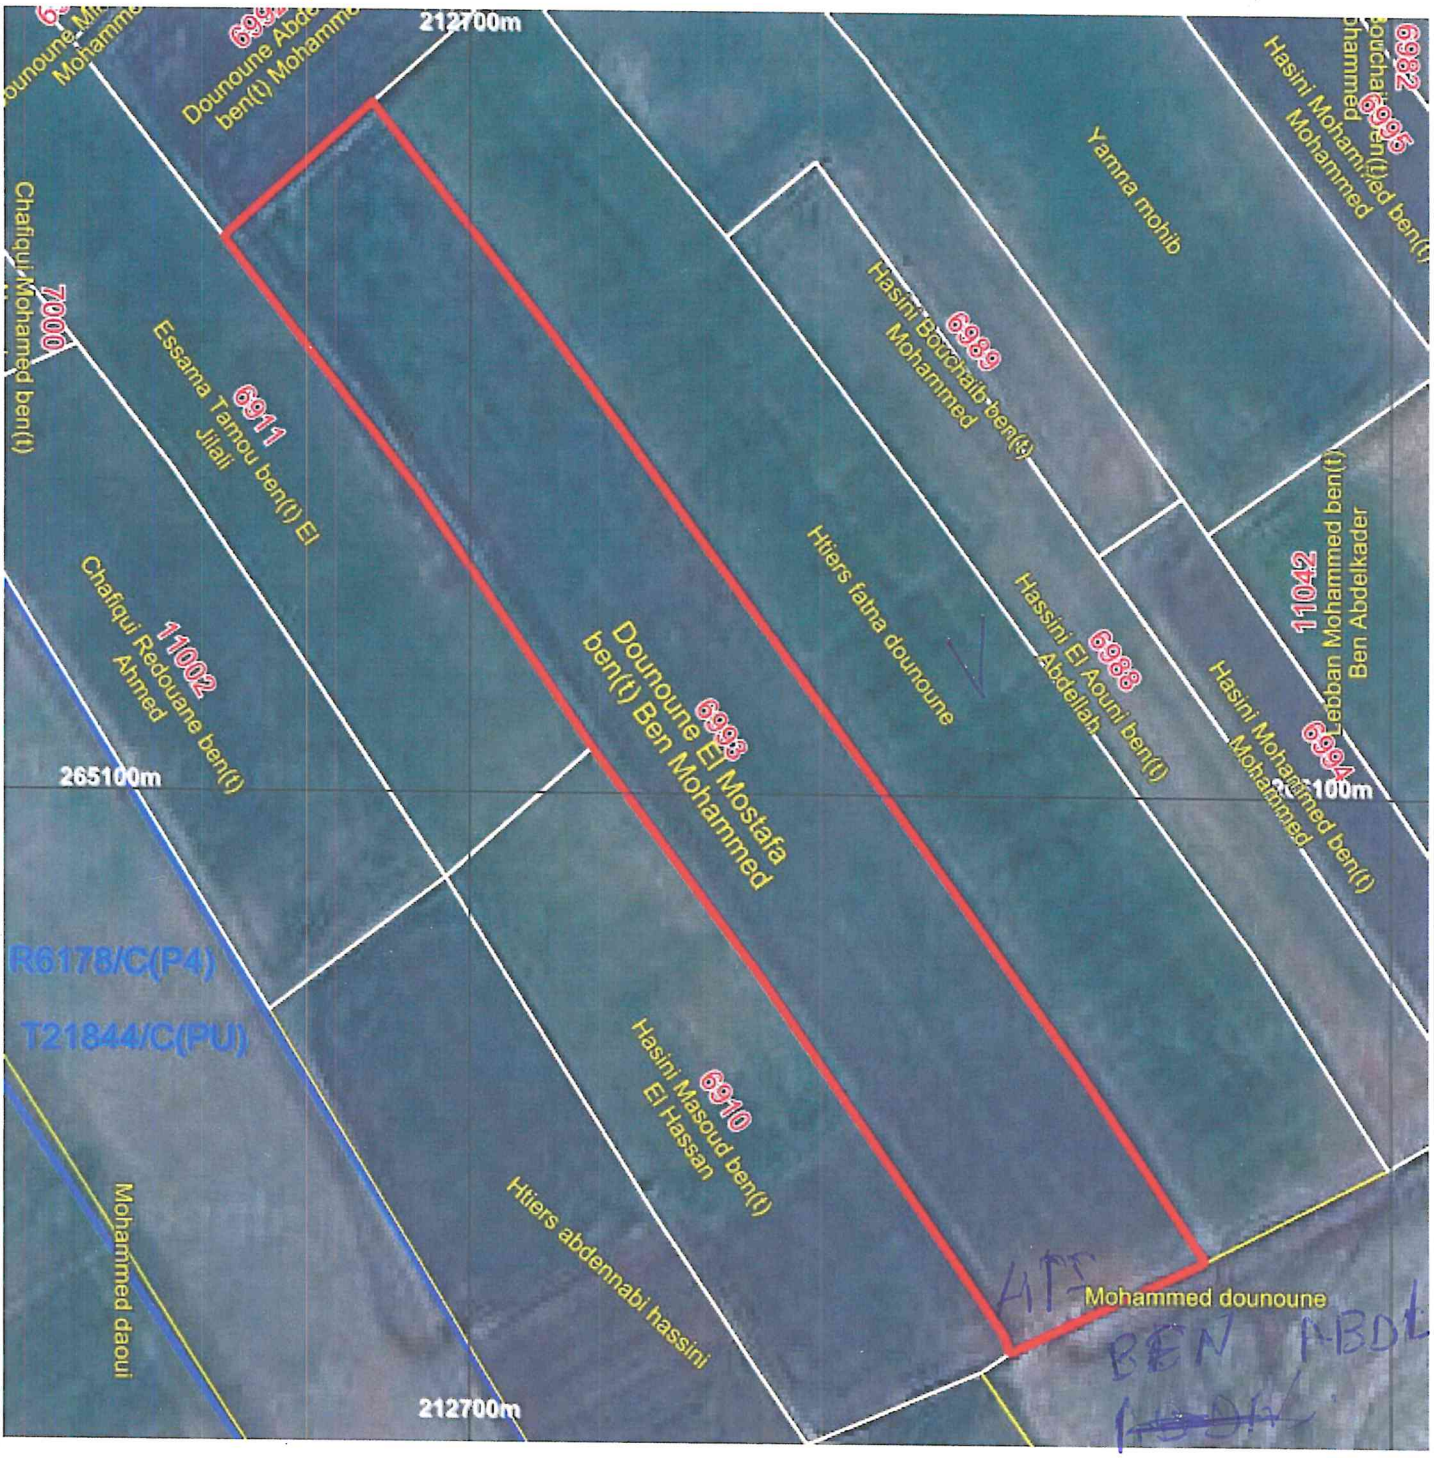

Mappe(1/2000)
23-12-99

Propriété dite : Ard Tres

Située à : Pce d'EL JADIDA, Cle de SIDI SMAIL, Cne. Mogress, Dr LAHRICHATE

Titre :

Echelle : 1/1000

Plan levé en : Mai 2025

Limite de la propriété

Réquisition N° :

ST 25

NORD الشمال

Plan Provisoire Avant enrôlement
Plle n° : 6993
IFE : Zone Mogress
Sous zone : 3

265200

265100

265000

212700

212800

v.B43197

v.B41852

Plle 6992 TC

B43210

B41853

B43211

Plle 6911 TC

B41854

B43212

Hiers Fatna Dounoune TC

TC

B41843

B43213

v.B41842

B41844

Plle 6910 TC

B43214

B43215

B41845

B41846

Mohammed Dounoune TC

v.B41847

Contenance : 33^A 89^Ca : مساحة

23-12-99-A

الملك المسمى : ارض تريس

الكائن ب : اقليم الجديدة دائرة سيدي اسماعيل جماعة مكرس دوار الحريشات

رسم :

مطلب عدد :

DIRECTION DU CADASTRE

Plan établi par : GEOXPER
Géomètre : MJOUEL Mohamed Amjad
Dessinateur : Automatique

MAPPE DE REPERAGE AU 1/2000 : 23-12-99
CARTE TOPOGRAPHIQUE DE SOUK ARBAA MOGRESS au 1/50000